



Pool Room — League Hall

Player-max: wall-to-wall tables, rail drinks only, no food

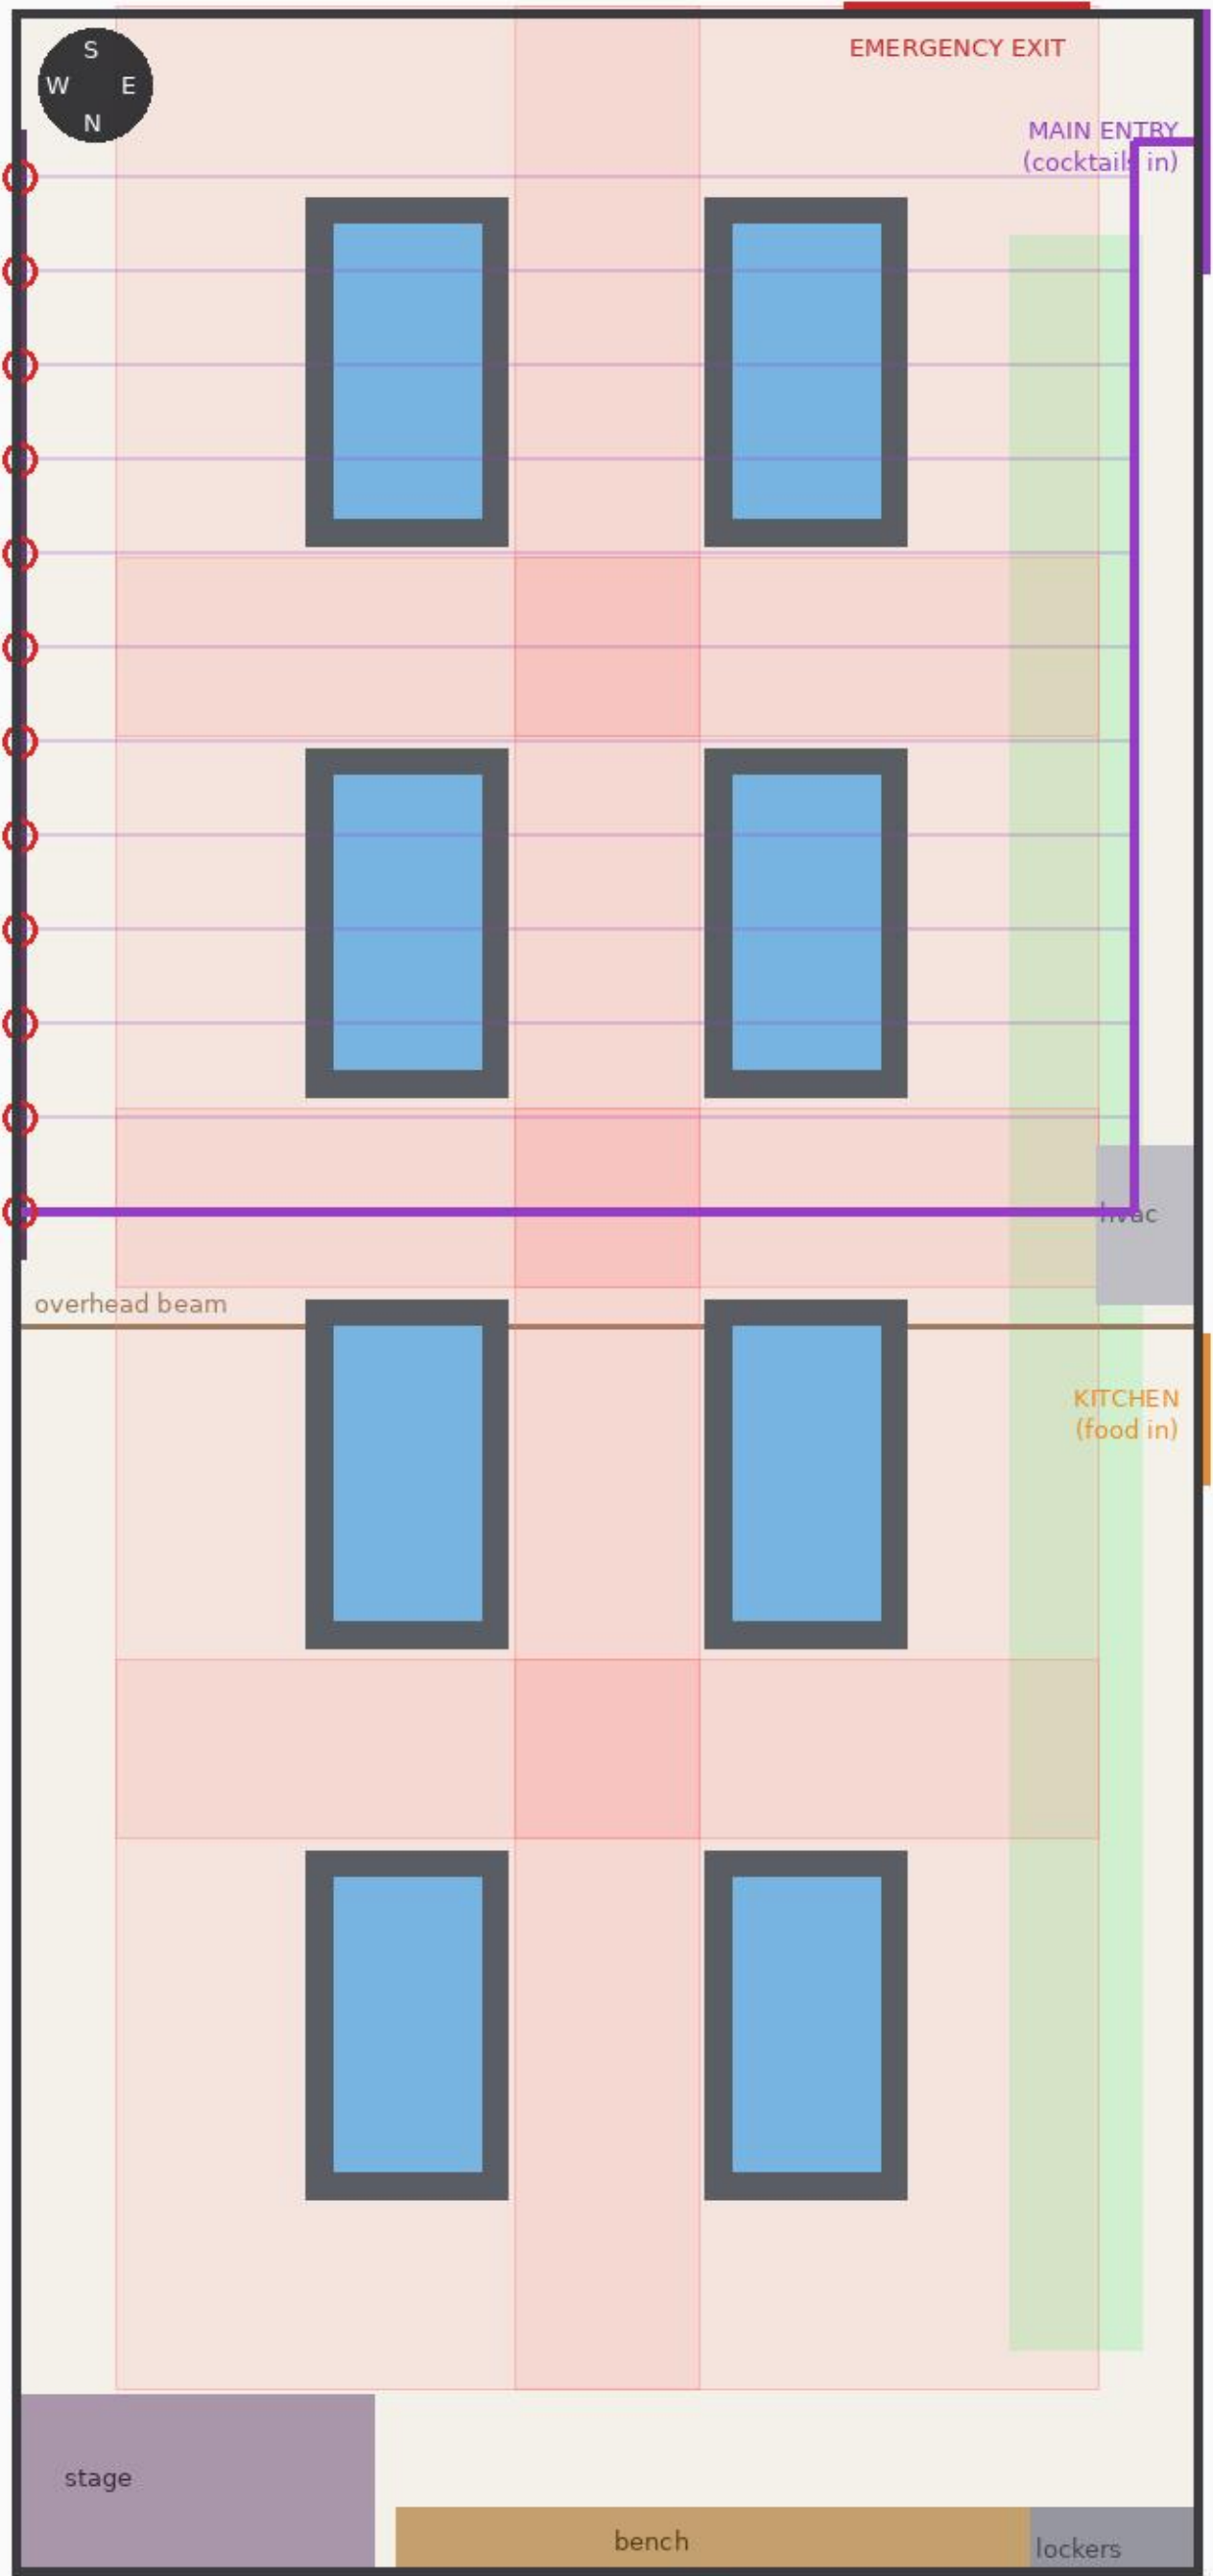

Pool Room — Social Hall (current)

The built layout: tables, classroom, and wall two-tops

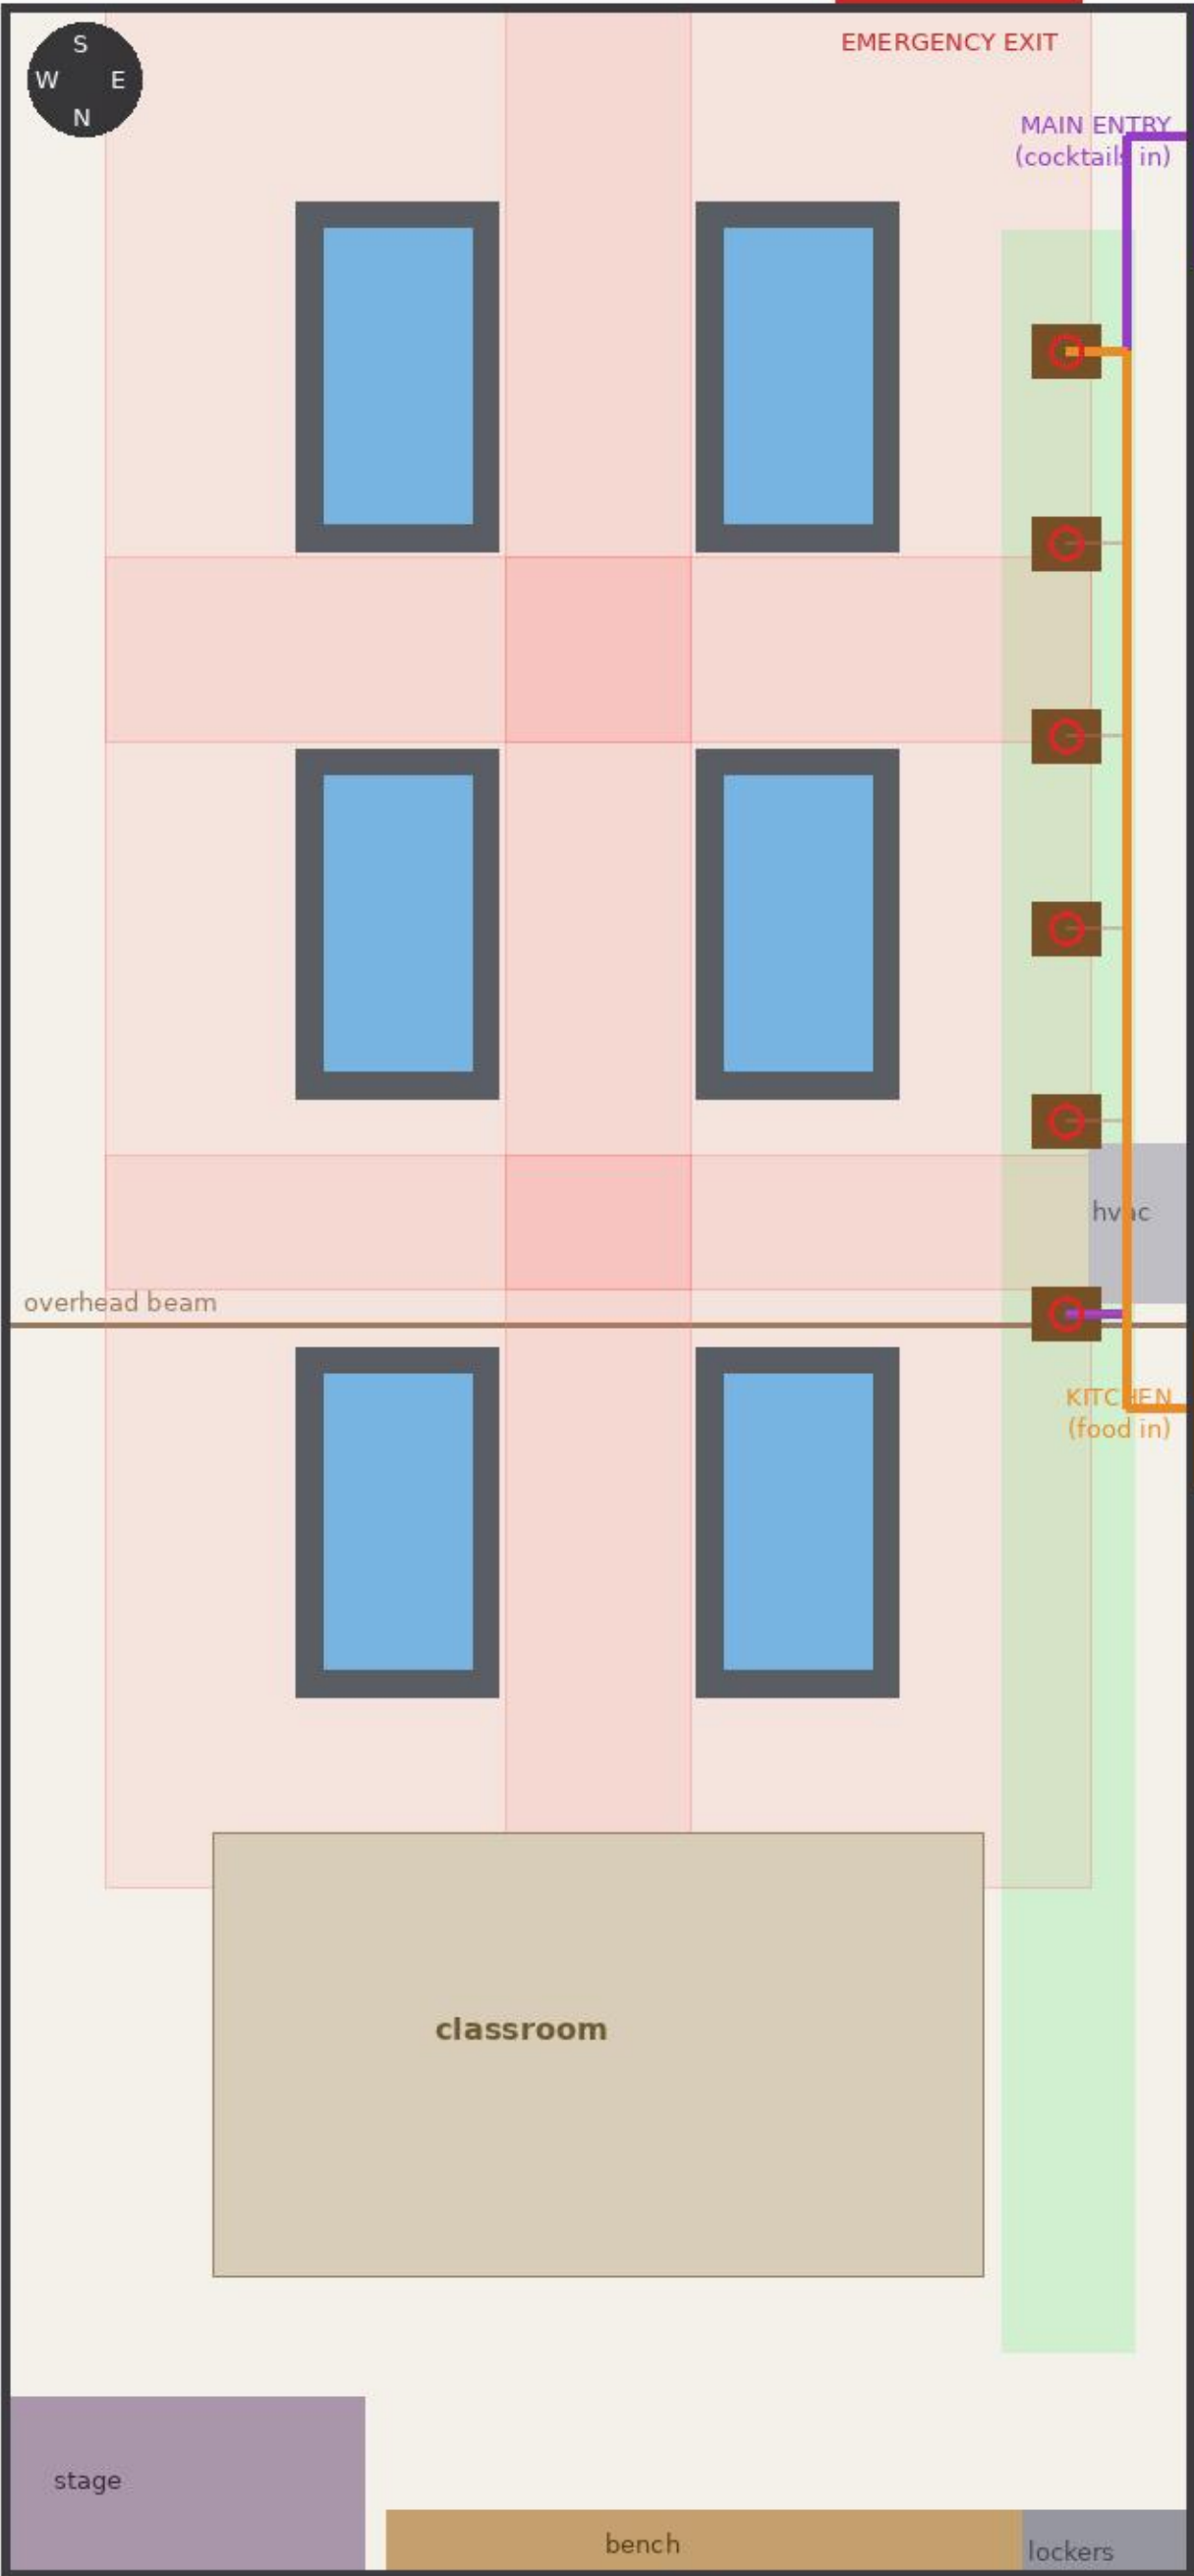

cocktail service

food service


cue-swing zone

Feature table with bleacher sightlines; stage becomes VIP




Pool Room — Cocktail Lounge

Bar-forward: high-top lounge and drink rails at the entry end

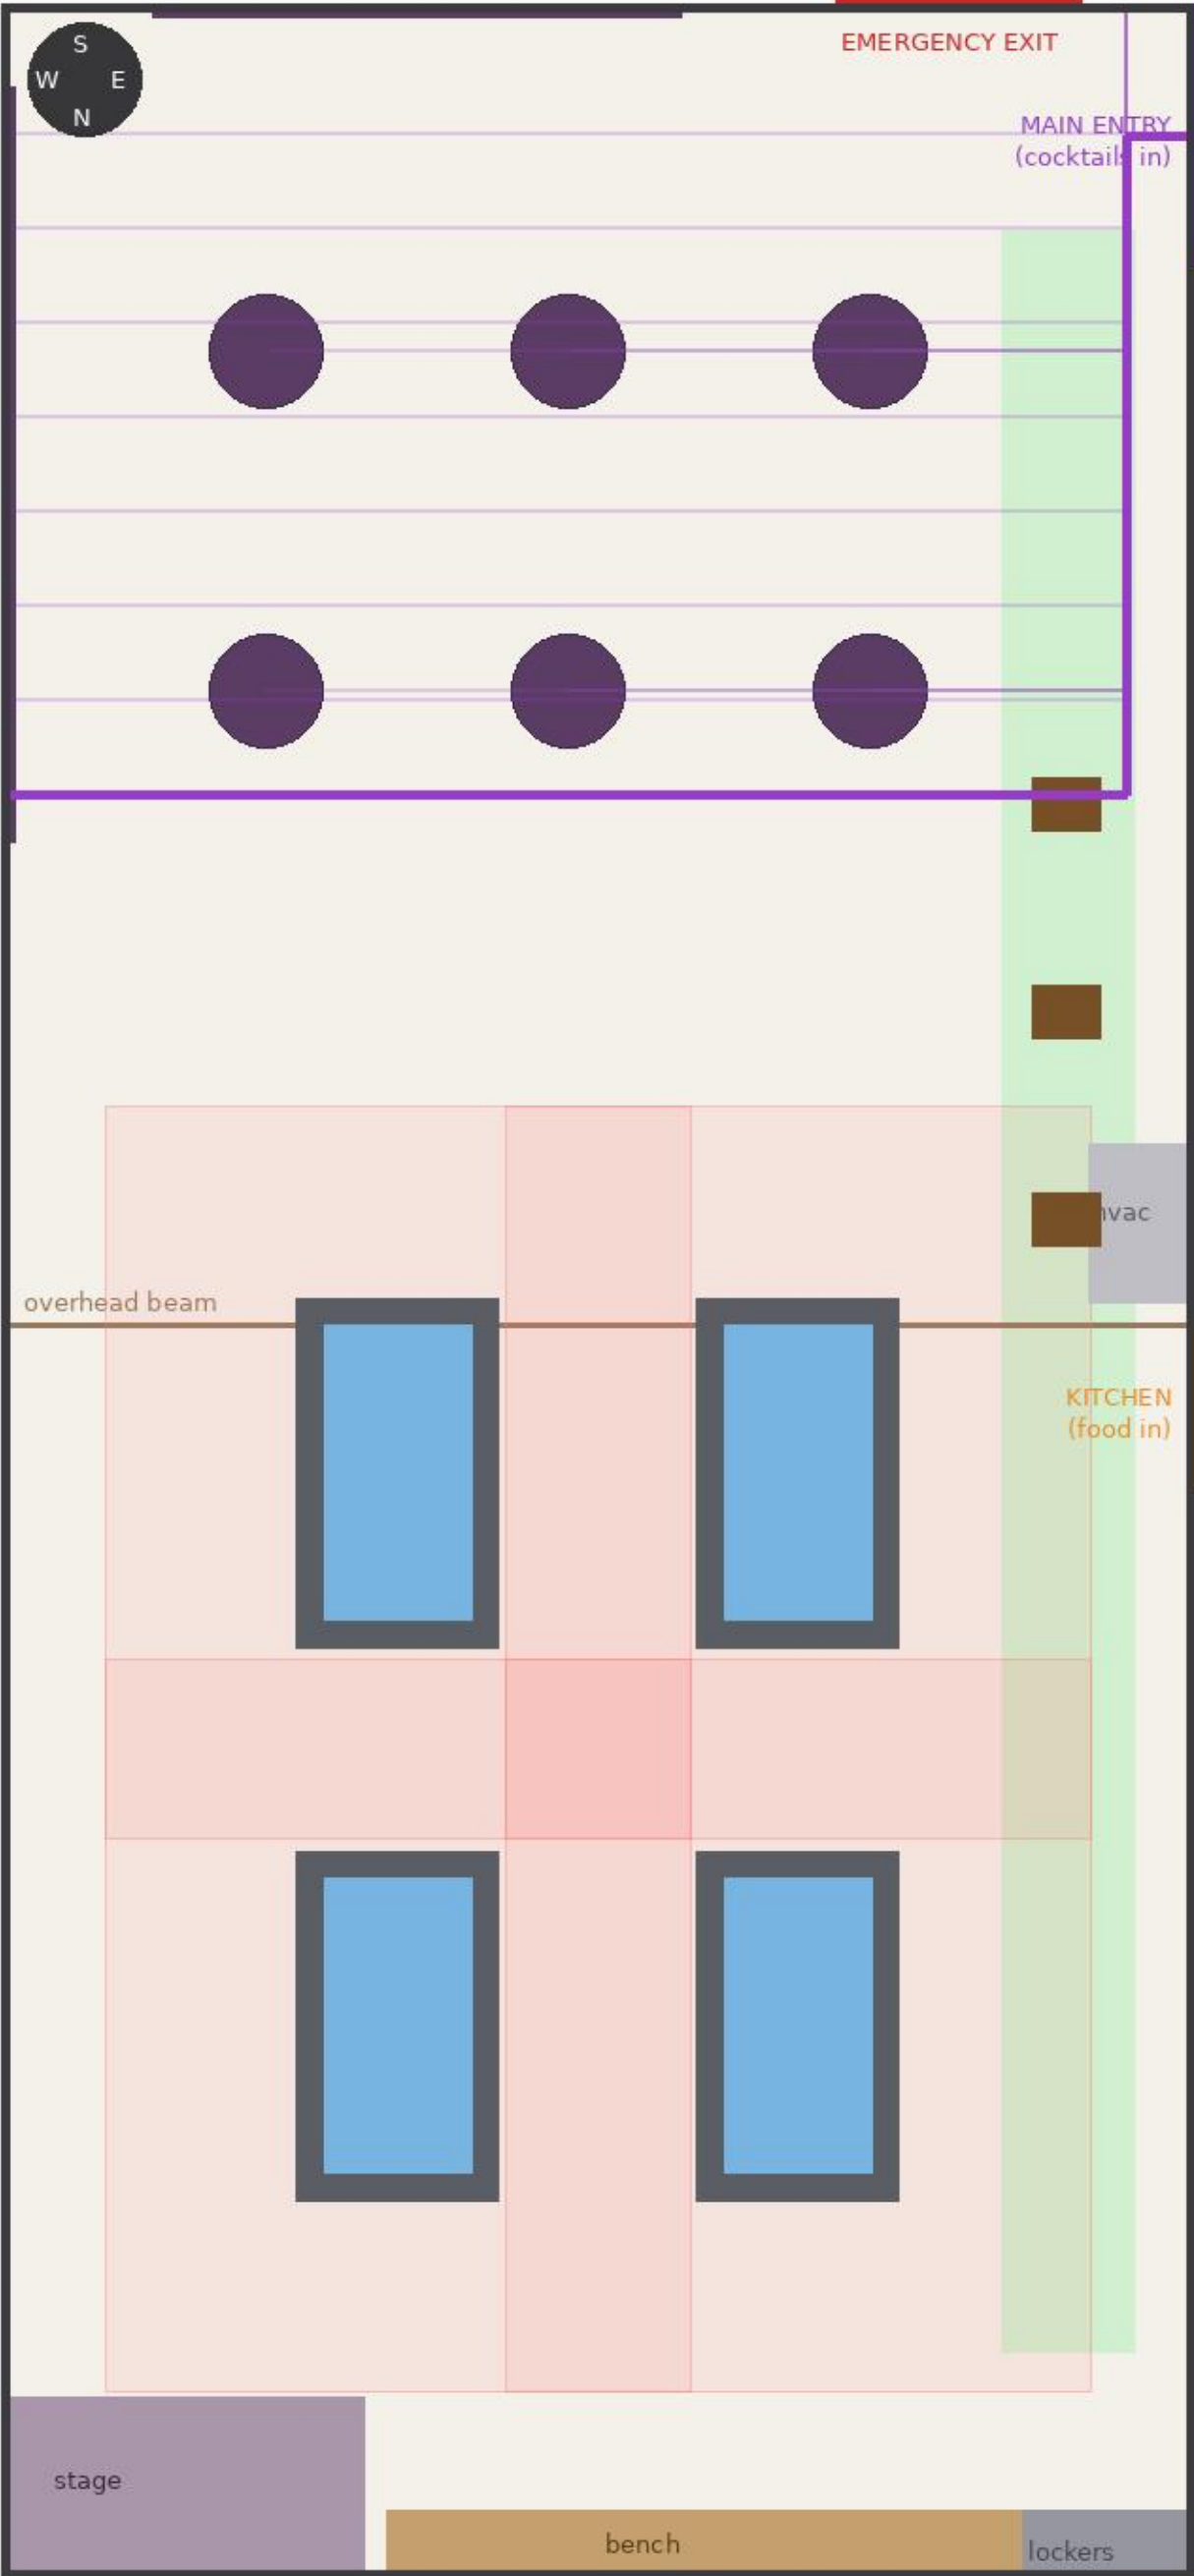


Pool Room — Billiards Bistro

Dining-forward: rounds wrap the kitchen door for a hot carry

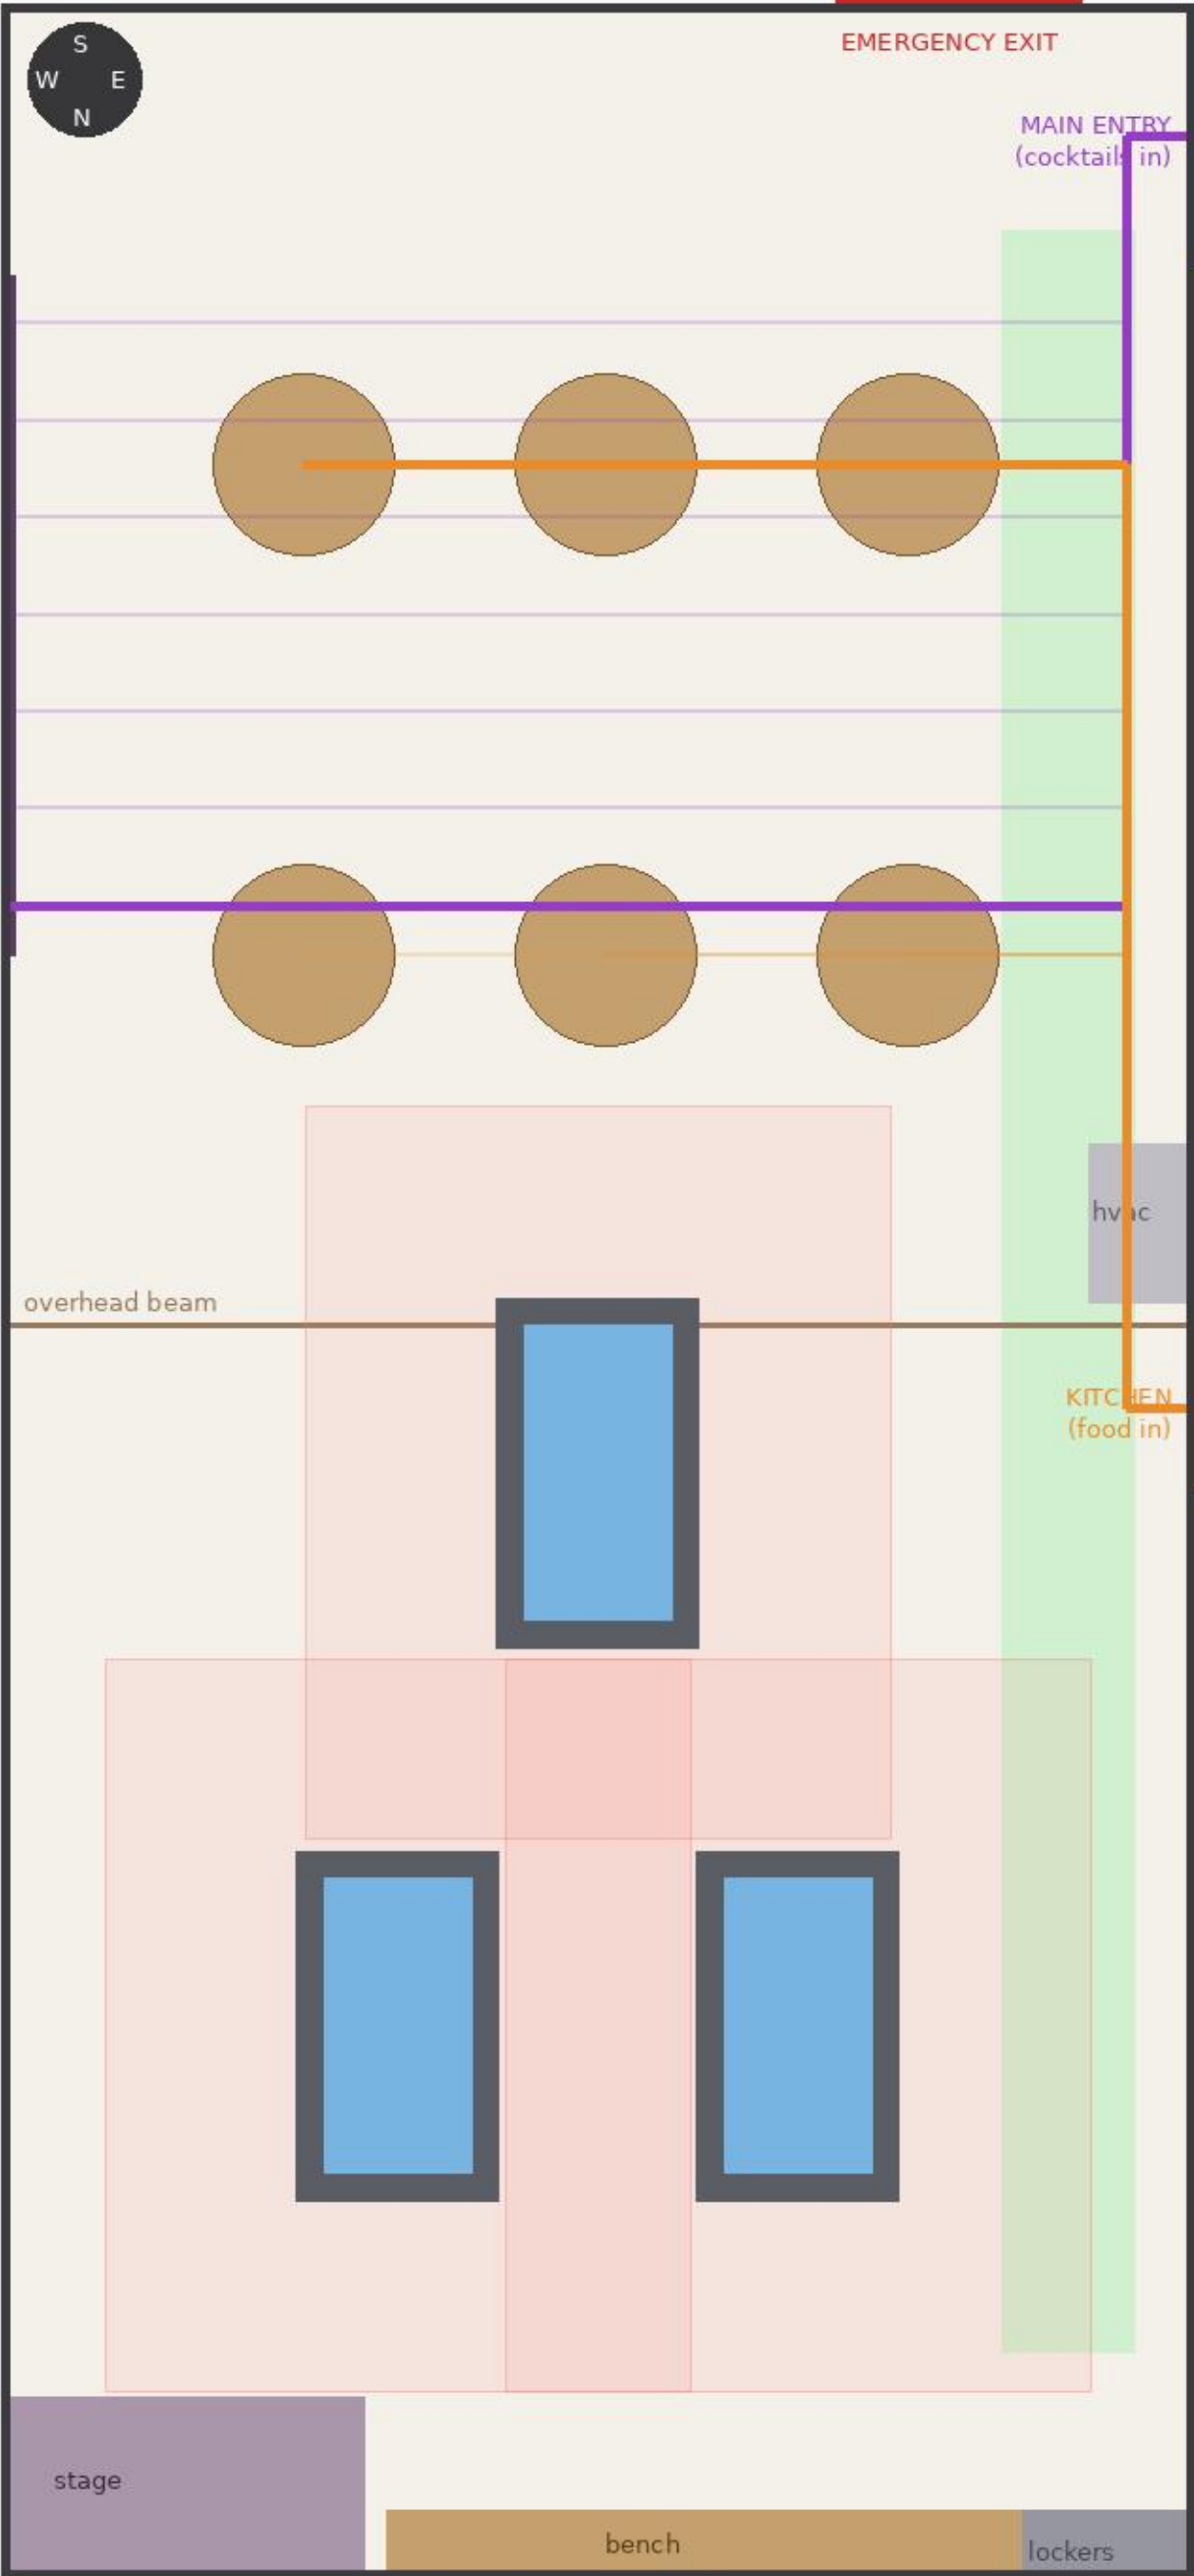

Pool Room — Split-House Flex

Beam line divides: fixed tables north, flex banquet south

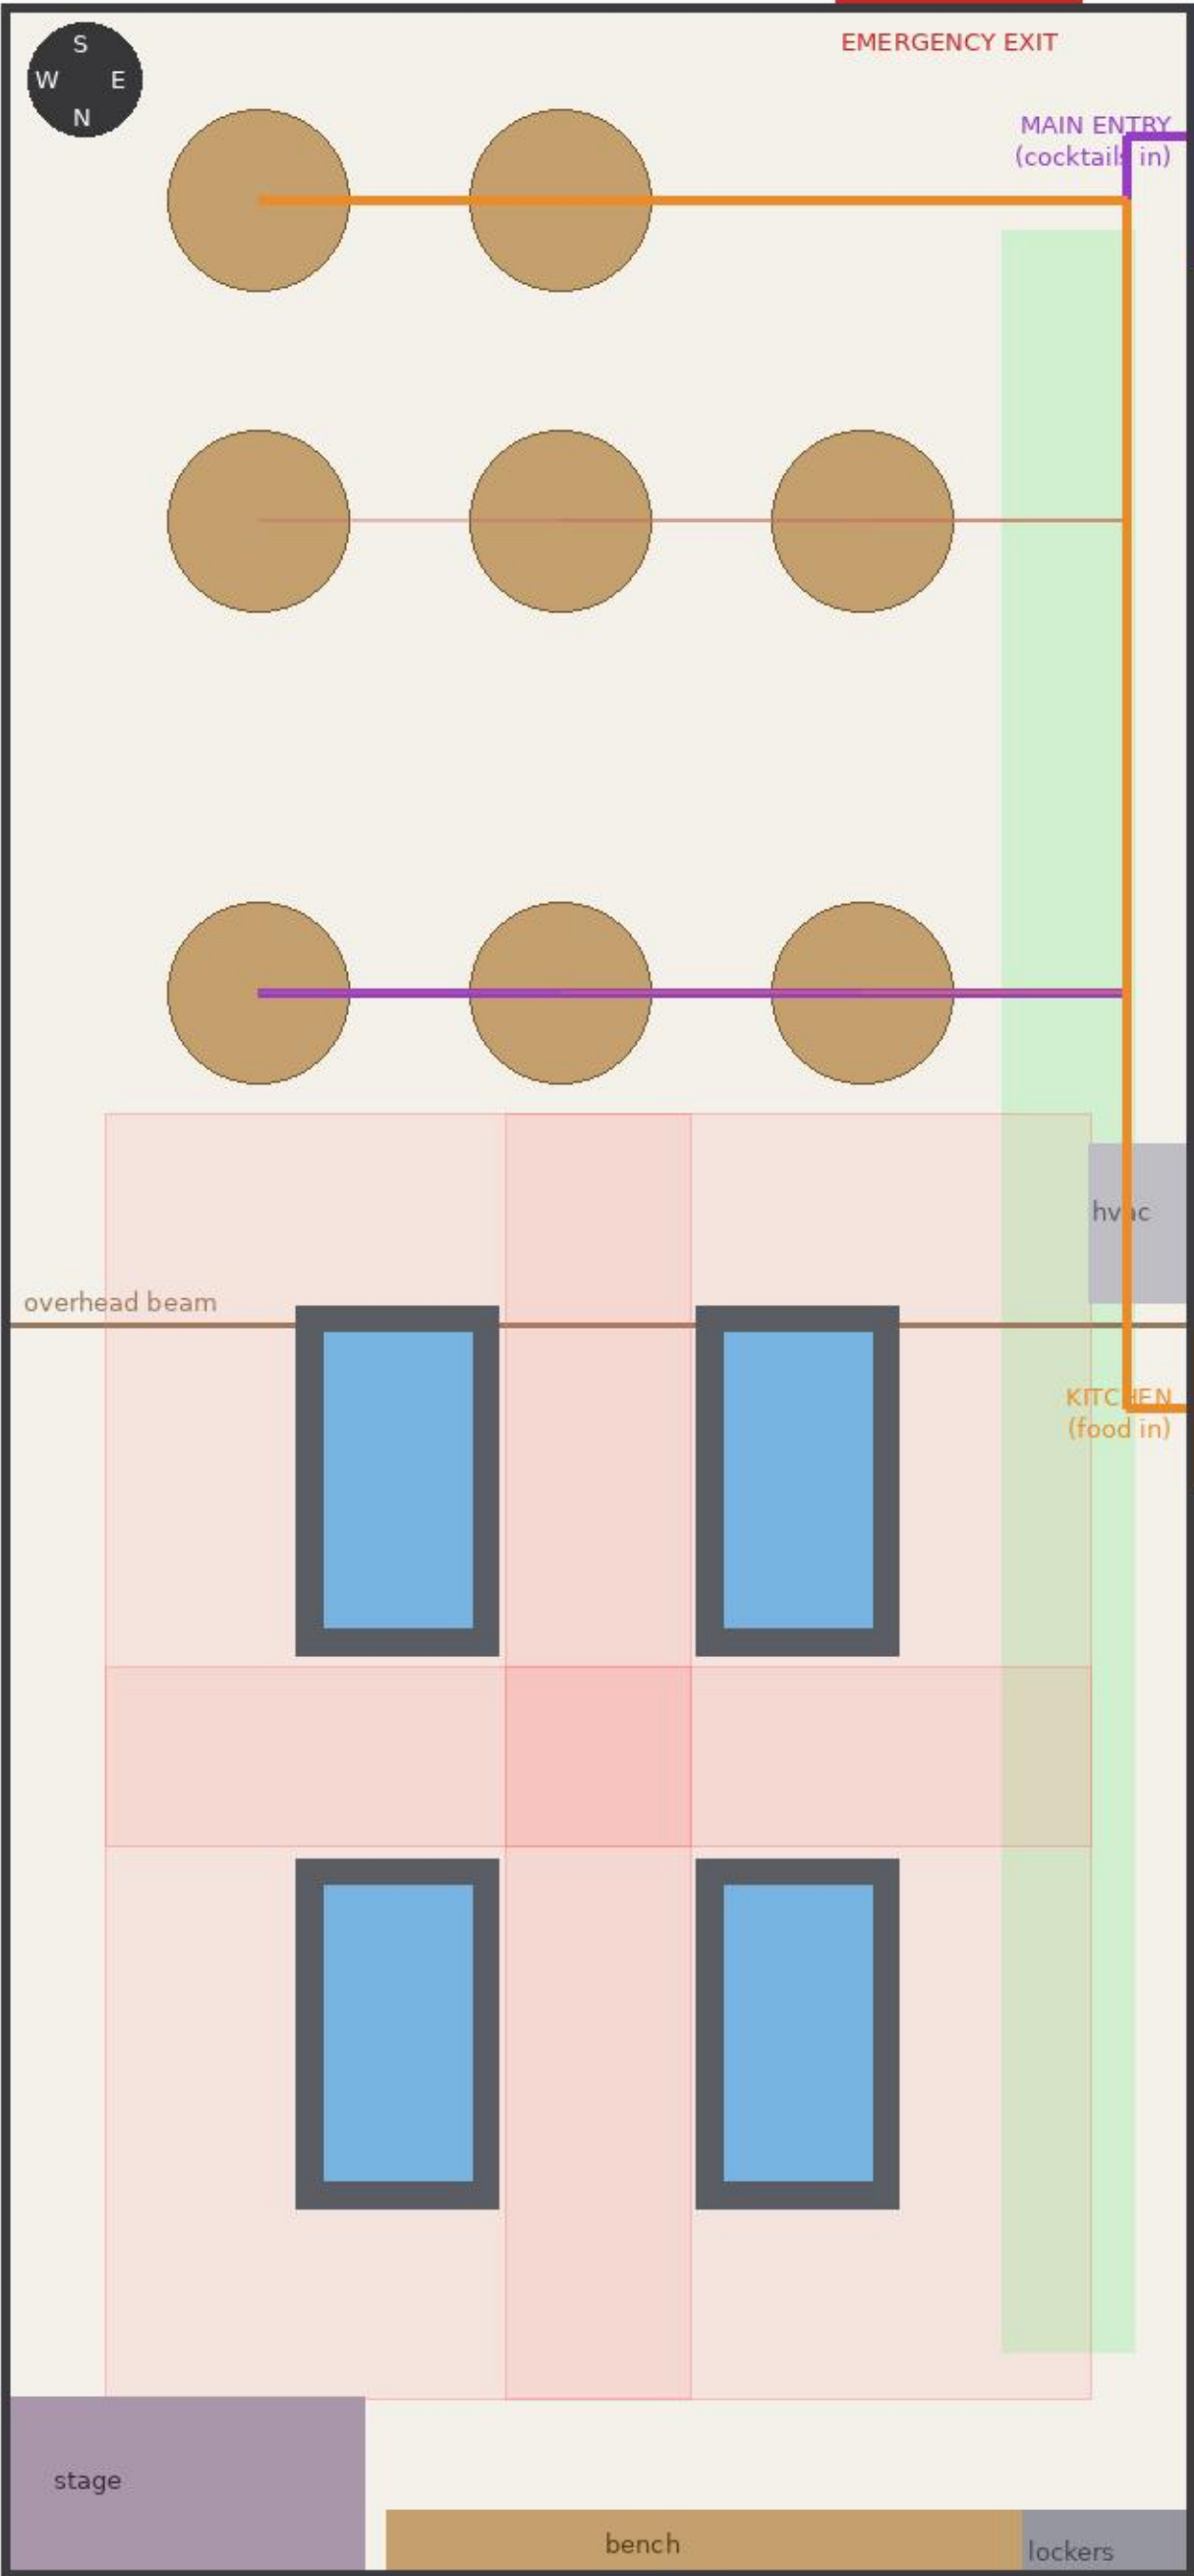

cocktail service

food service

cue-swing zone